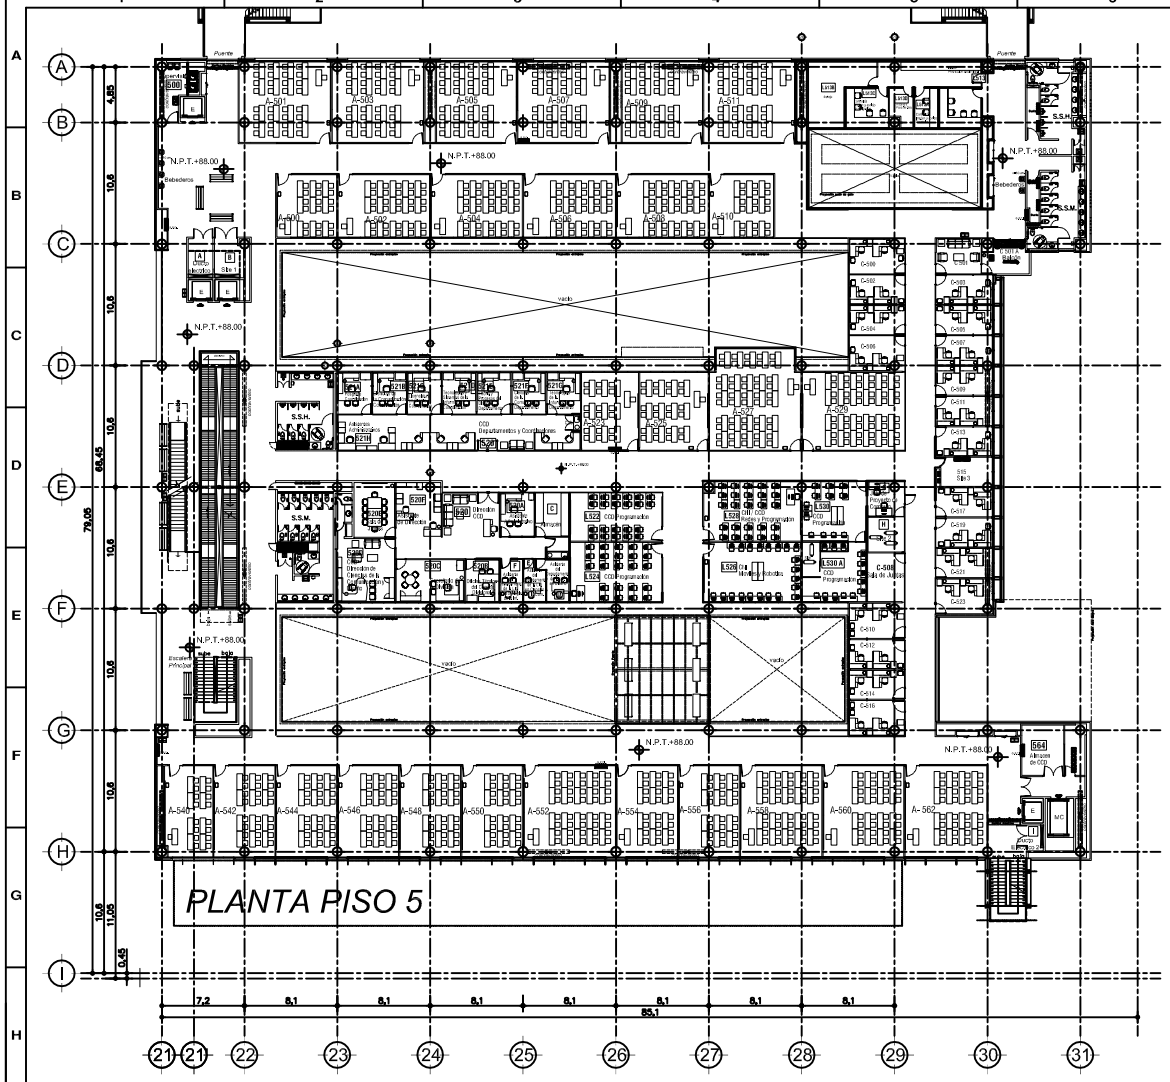

TORRE III
5° PISO
4,552.00 M2 (c)

500. Supervisión

Aulas

A-500
A-501
A-502
A-503
A-504
A-505
A-506
A-507
A-508
A-509
A-510
A-511
A-523
A-525
A-527
A-529
A-540
A-542
A-544
A-546
A-548
A-550
A-552
A-554
A-556
A-558
A-560
A-562

L 513. CCD Master de Producción Audiovisual
- **L 513 A.** Control de imagen y sonido / Docencia
- **L 513 B.** Bodega
- **L 513 C.** Control de imagen y sonido / Investigación
- **L 513 D.** Acceso a paso de Gato

520. CCD Dirección
- **520 A.** Asistente administrativo
- **520 B.** Consejo Divisional / Oficina Técnica
- **520 C.** Secretaría Académica/ División
- **520 D.** Ciencias de la Comunicación y Diseño / Dirección
- **520 E.** Sala de Juntas
- **520 F.** Asistente de Dirección

521. CCD / Departamentos y Coordinaciones
- **521 A.** Posgrado Coordinación
- **521 B.** Ciencias de la Comunicación / Coordinación
- **521 C.** Diseño / Coordinación
- **521 D.** Tecnologías y Sistemas de la Información / Coordinación
- **521 E.** Teoría y Procesos del Diseño / Departamento
- **521 F.** Ciencias de la Comunicación / Departamento
- **521 G.** Tecnologías de la Información / Departamento
- **521 H.** Asistentes de Coordinación

Laboratorios
- **L 522.** CCD Programación
- **L 524.** CCD Programación
- **L 526.** CNI Móviles y Robótica
- **L 528.** CNI / CCD Redes y Programación
- **L 530.** CCD Programación
  - **L 530 A.** CCD Programación

564. CCD Bodega

Cubículos de Profesores

C 500
C 501
501-A
C 502
C 503
C 504
C 505
C 506
C 507
C 508.
C 509
C 510
C 511
C 512
C 513
515.
C 514
C 515
C 516
C 517
C 519
C 521
C 523

A. Ducto eléctrico 1
B. Site 1
C. Almacen
D. Asistente del Depto. en Diseño
E. Asistente del Depto. en Comunicación
F. Asistente del Depto. de Tecnologías
G. Jefe de Proyecto de Cómputo
H. Site 2
I. Ducto Eléctrico 2

SIMBOLOGIA

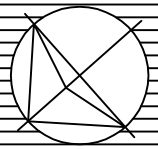

NOTAS GENERALES

- N. NIVEL
- N.P.T. NIVEL DE PISO TERMINADO
- N.L.B.F. NIVEL LECHO BAJO DE FALDÓN
- N.L.A.L. NIVEL LECHO ALTO DE LOSA
- N.L.B.L. NIVEL LECHO BAJO DE LOSA
- N.P.RETILP. NIVEL DE PRETIL DE PREFABRICADO
- N.P.RETILC. NIVEL DE PRETIL DE CONCRETO
- N.L.B.PL. NIVEL LECHO BAJO DE PLAFÓN

1. LAS COTAS RIGEN AL DIBUJO.
2. LAS COTAS ESTÁN DADOS EN METROS.
3. LAS COTAS Y NIVELES SE VERIFICARÁN EN OBRA.

No	REVISION	FECHA	APROBO
1	EMITIDO P/CONSTRUCCION	16/MAR/12	J.L.R.O.
2	ACTUALIZACIÓN	01/SEP/15	G.A.A/A.F.S
3			
4			
5			
6			
7			
8			

Tamaño de plantar			60 x 90 cm
Código de colores (AUTOCAD 2006)			
AZUL, 132	0.40	34,54,66,75	0.10 COLOR
VERDE	0.20	76,96,96	0.10 COLOR
8 AL 9	0.10 EN B	105,119	0.10 COLOR
250 AL 255	0.10 EN B	Otro	0.05

LOCALIZACIÓN

PLANTA DE CONJUNTO

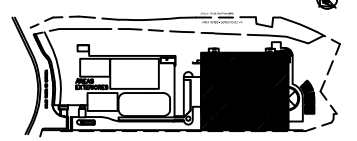

CORTE TRANSVERSAL

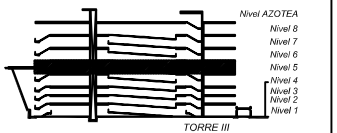

Casa abierta al tiempo

DR. ENRIQUE FERNANDEZ FASSNACHT
RECTOR GENERAL
DR. ARTURO ROJO DOMINGUEZ
RECTOR DE LA UNIDAD CUAJIMALPA
MTRA. IRIS EDITH SANTACRUZ FABILA
SECRETARIO GENERAL
MTRO. GERARDO QUIROZ VIEYRA
SECRETARIA DE LA UNIDAD CUAJIMALPA

UNIVERSIDAD AUTONOMA METROPOLITANA
UNIDAD CUAJIMALPA
NUEVA SEDE UAM CUAJIMALPA
TORRE III

PROPIETARIO: UNIVERSIDAD AUTONOMA METROPOLITANA
DIRECCIÓN: AV VASCO DE QUIROGA No. 4871 COL. SANTA FE, CUAJIMALPA DE MORELOS, MÉXICO D.F.

PLANO ARQUITECTONICO / PISO 1		clave	A-R
ARQUITECTONICO			A-05
OBRA NUEVA	escala 1:200		
fecha SEPT – 15	dibujo ARQ. GOA/AFG		

Grupo Frase S.A. de C.V.
Arq. Ramiro Ortiz Trevilla — Arq. Raúl Kabah Hadane